BEWEHRUNG DECKE Ü. ERDGESCHOSS M 1:50

obere Lage

Matten örtlich oder im Werk zuschneiden lassen, Q335A Stöße ≥ 35 cm

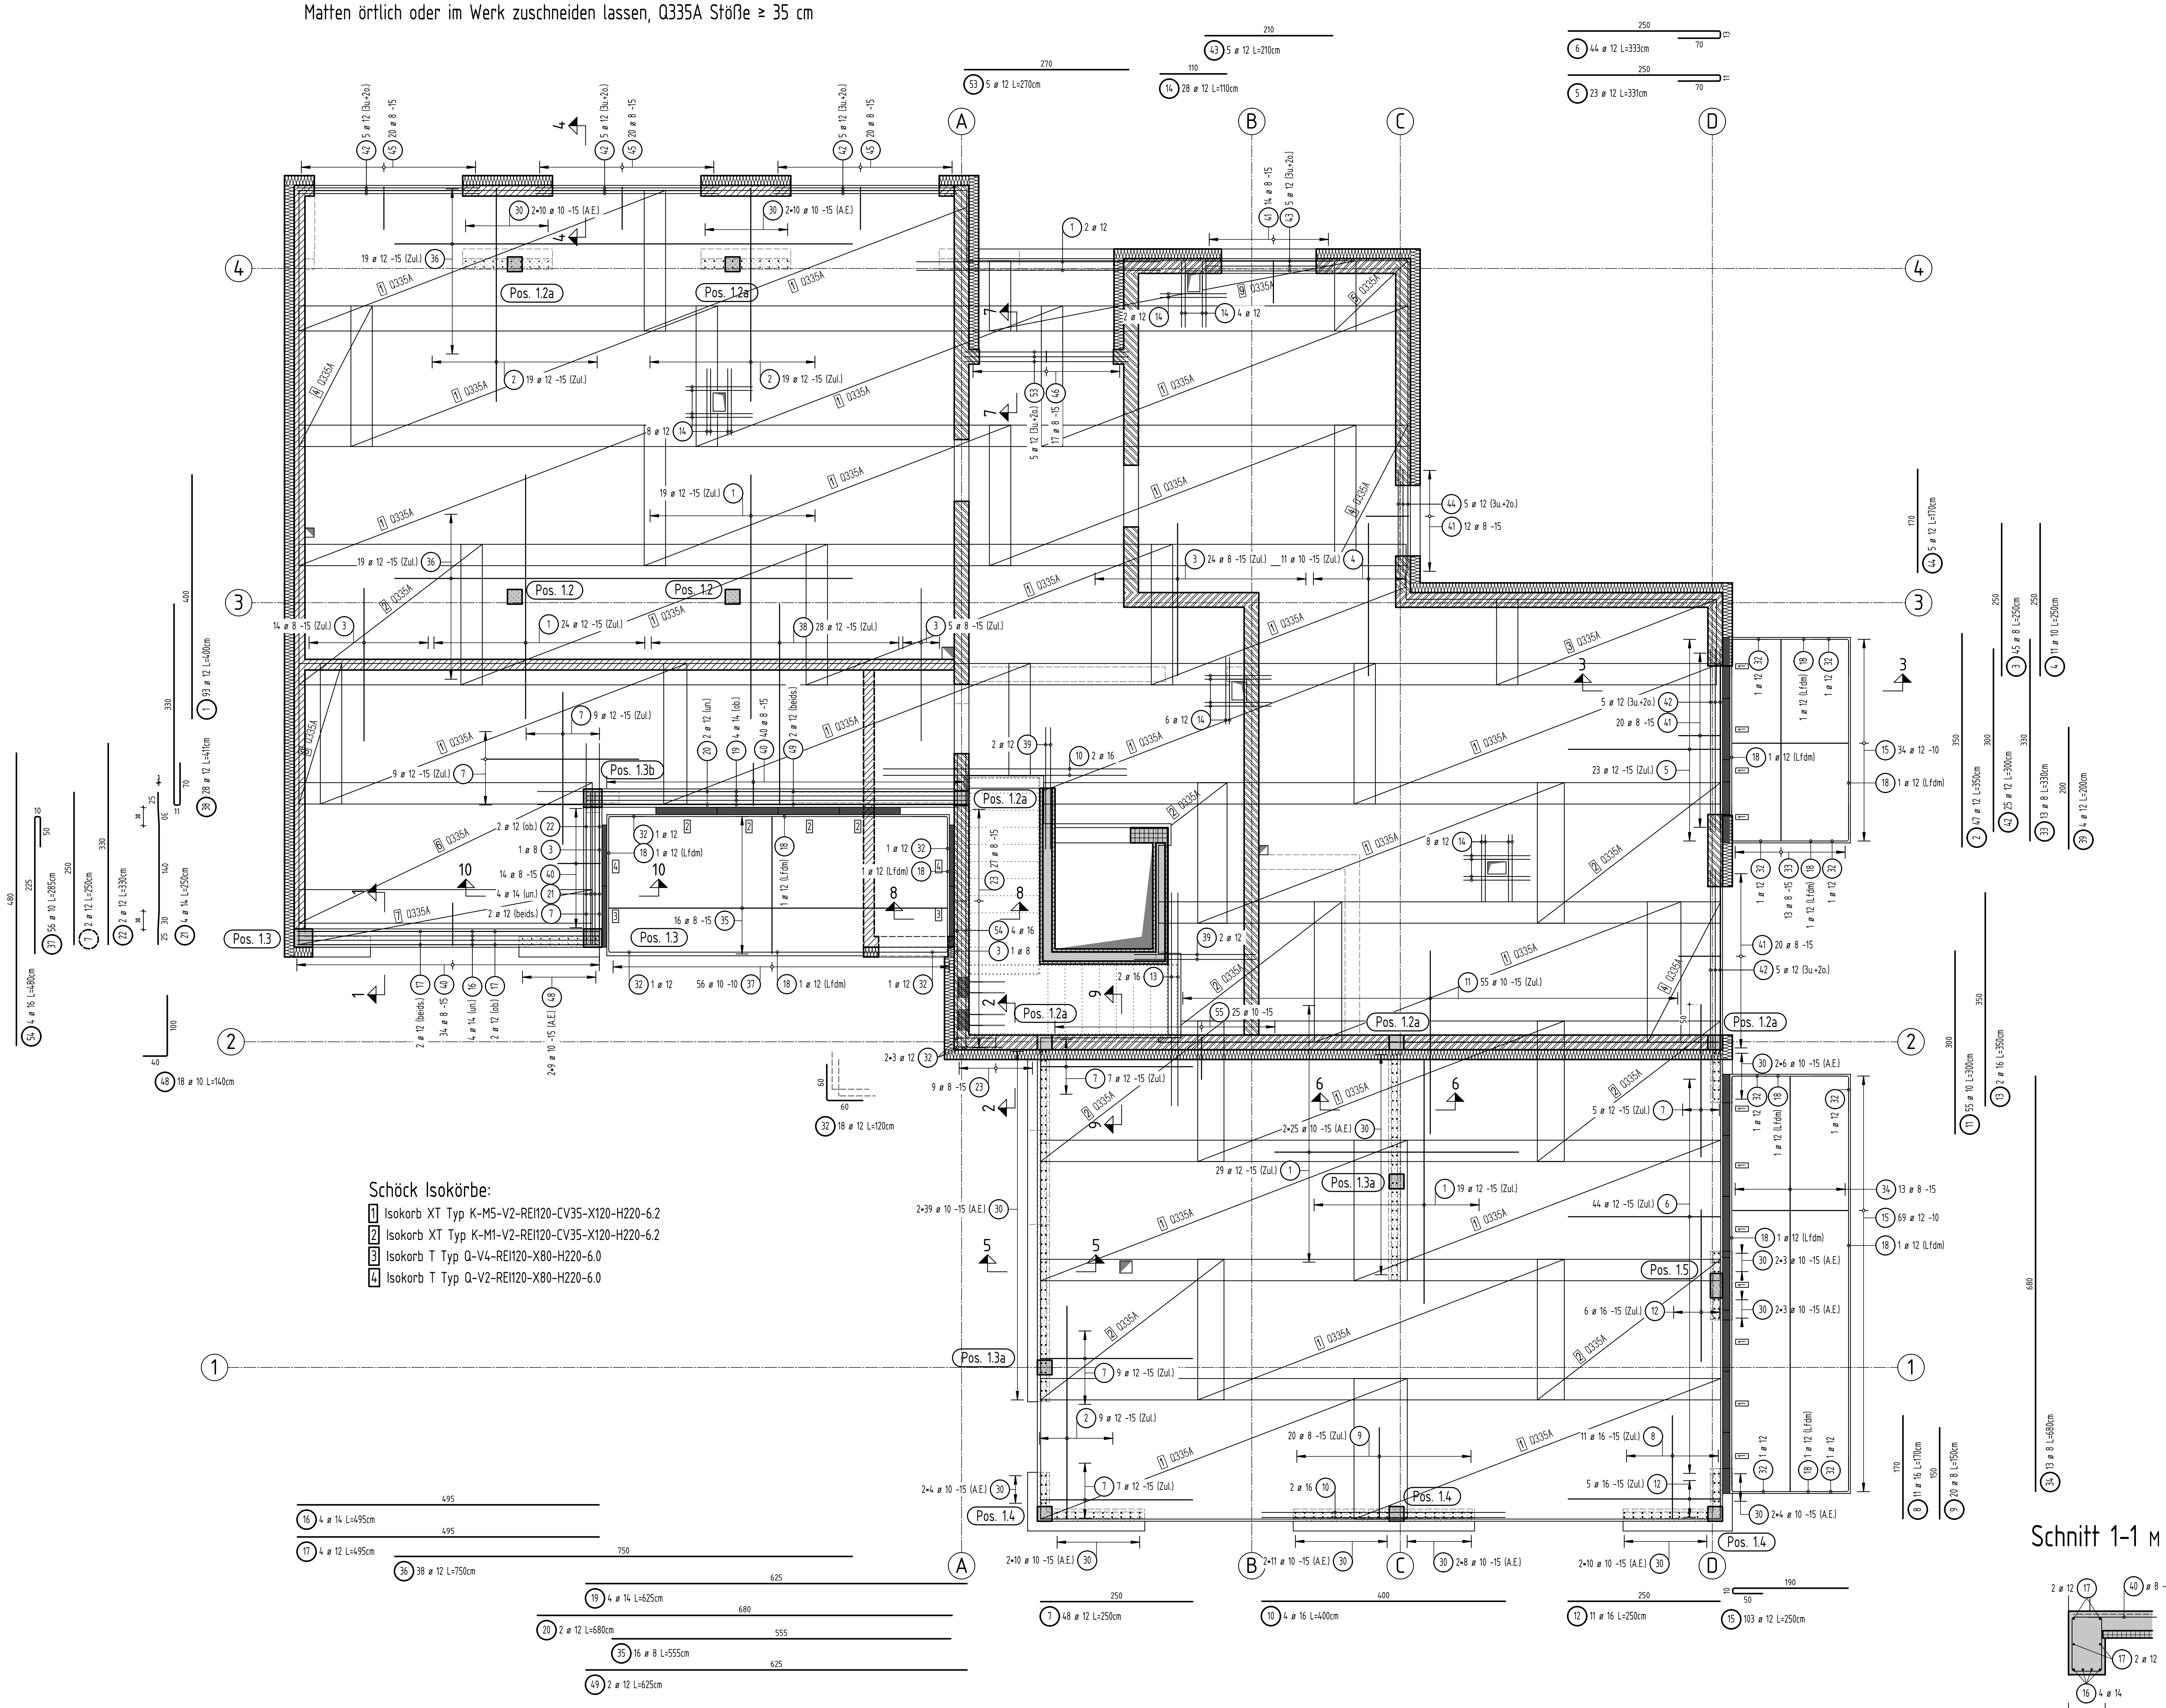

Schöck Isokörbe:

1 Isokorb XT Typ K-M5-V2-REI120-CV35-X120-H220-6.2
2 Isokorb XT Typ K-M1-V2-REI120-CV35-X120-H220-6.2
3 Isokorb T Typ Q-V4-REI120-X80-H220-6.0
4 Isokorb T Typ Q-V2-REI120-X80-H220-6.0

Stabliste - Biegeformen

Pos.	Stck	ø [mm]	Einzel Länge [m]	Bemaßte Biegeform (unmaßstäblich)	Gesamt Länge [m]	Masse [kg]
1	93	12	4.00	400	372.00	330.34
2	47	12	3.50	350	164.50	146.08
3	45	8	2.50	250	112.50	44.44
4	11	10	2.50	250	27.50	16.97
5	23	12	3.31	250 11 70	76.13	67.60
6	44	12	3.33	250 13 70	146.52	130.11
7	48	12	2.50	250	120.00	106.56
8	11	16	1.70	170	18.70	29.55
9	20	8	1.50	150	30.00	11.85
10	4	16	4.00	400	16.00	25.28
11	55	10	3.00	300	165.00	101.80
12	11	16	2.50	250	27.50	43.45
13	2	16	3.50	350	7.00	11.06
14	28	12	1.10	110	30.80	27.35
15	103	12	2.50	190 10 50	257.50	228.66
16	4	14	4.95	495	19.80	23.96
17	4	12	4.95	495	19.80	17.58
18	1	12	Lfdm		105.00	93.24
19	4	14	6.25	625	25.00	30.25
20	2	12	6.80	680	13.60	12.08
21	4	14	2.50	30 140 3 30 25 30 25 30	10.00	12.10
22	2	12	3.30	330	6.60	5.86
23	36	8	0.95	19 12 17	34.20	13.51
24	84	12	2.95	295	247.80	220.05
25	130	8	0.91	17 12 17	118.30	46.73
26	72	8	1.23	25 12 25	88.56	34.98
27	32	12	1.50	150	48.00	42.62
28	36	14	2.95	295	106.20	128.50
29	26	8	1.15	13 12 33	29.90	11.81
30	286	10	1.20	40 80	343.20	211.75
31	2	12	1.50	30 120	3.00	2.66
32	18	12	1.20	60 60	21.60	19.18
33	13	8	3.30	330	42.90	16.95
34	13	8	6.80	680	88.40	34.92
35	16	8	5.55	555	88.80	35.08
36	38	12	7.50	750	285.00	253.08
37	56	10	2.85	50 10 225	159.60	98.47
38	28	12	4.11	70 11 330	115.08	102.19
39	4	12	2.00	200	8.00	7.10
40	88	8	1.97	1270 45 45 25	173.36	68.48
41	66	8	1.31	70 12 15 15 19	86.46	34.15
42	25	12	3.00	300	75.00	66.60
43	5	12	2.10	210	10.50	9.32
44	5	12	1.70	170	8.50	7.55
45	60	8	1.22	70 12 14 14 13	73.20	28.91
46	17	8	0.91	19 12 15	15.47	6.11
47	208	8	0.99	19 12 19	205.92	81.34
48	18	10	1.40	100 40	25.20	15.55
49	2	12	6.25	625	12.50	11.10
50	16	12	3.70	30 3 70 30 270	59.20	52.57
51	24	12	2.95	30 3 50 30 215	70.80	62.87
52	10	8	0.36	12 13 12	3.60	1.42
53	5	12	2.70	270	13.50	11.99
54	4	16	4.80	480	19.20	30.34
55	25	10	1.53	70 13	38.25	23.60

Gesamtmasse : 3307.65

Matten- Schneideskizze

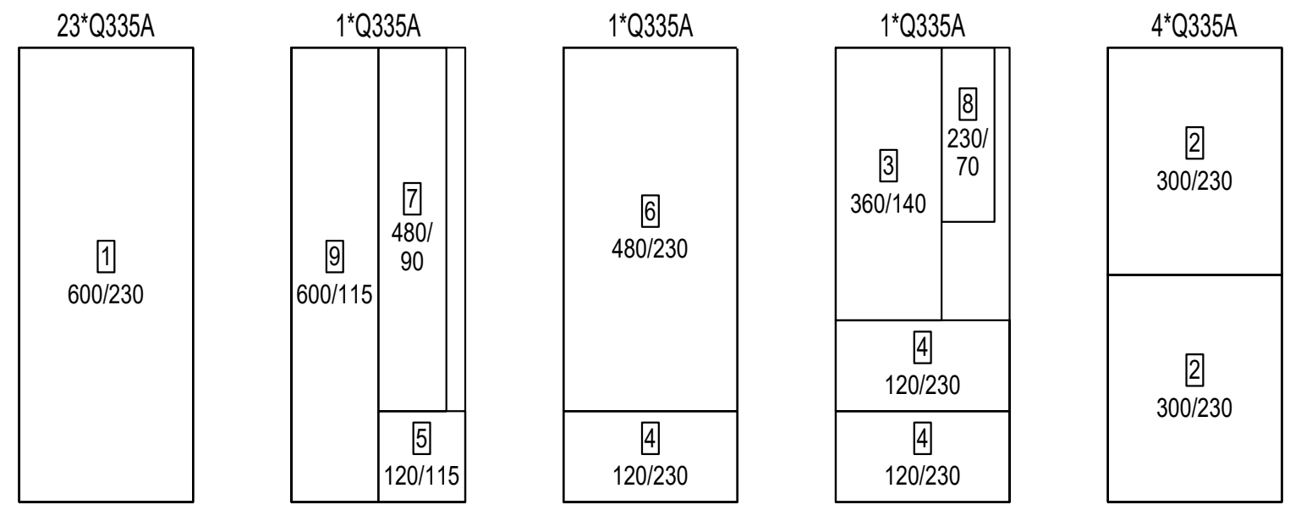

Stück	Bezeichnung	Brutto[kg]	Netto
30	Q335A	2229.00	2213.76
30	Summe	2229.00	2213.76

Bauteil	Expositions-klasse	Beton	E-Modul	nom c	Überwachungs-klasse (ÜK)
Decke über EG Unterzug	XC1	C25/30	31000 N/mm²	innen 2,5 mm aussen 3,5 mm	1
Balkon	XC4, XF1	C25/30	31000 N/mm	allseitig 4,0 mm	1
Aussenstütze	XC3, WF	C25/30	31000 N/mm²	allseitig 3,5 mm	1
Innenstütze	XC1	C25/30	31000 N/mm²	allseitig 2,5 mm	1

Pos. 1.2 Stb.-Stützen

b/d = 24/24cm M 1:25

2x ausführen

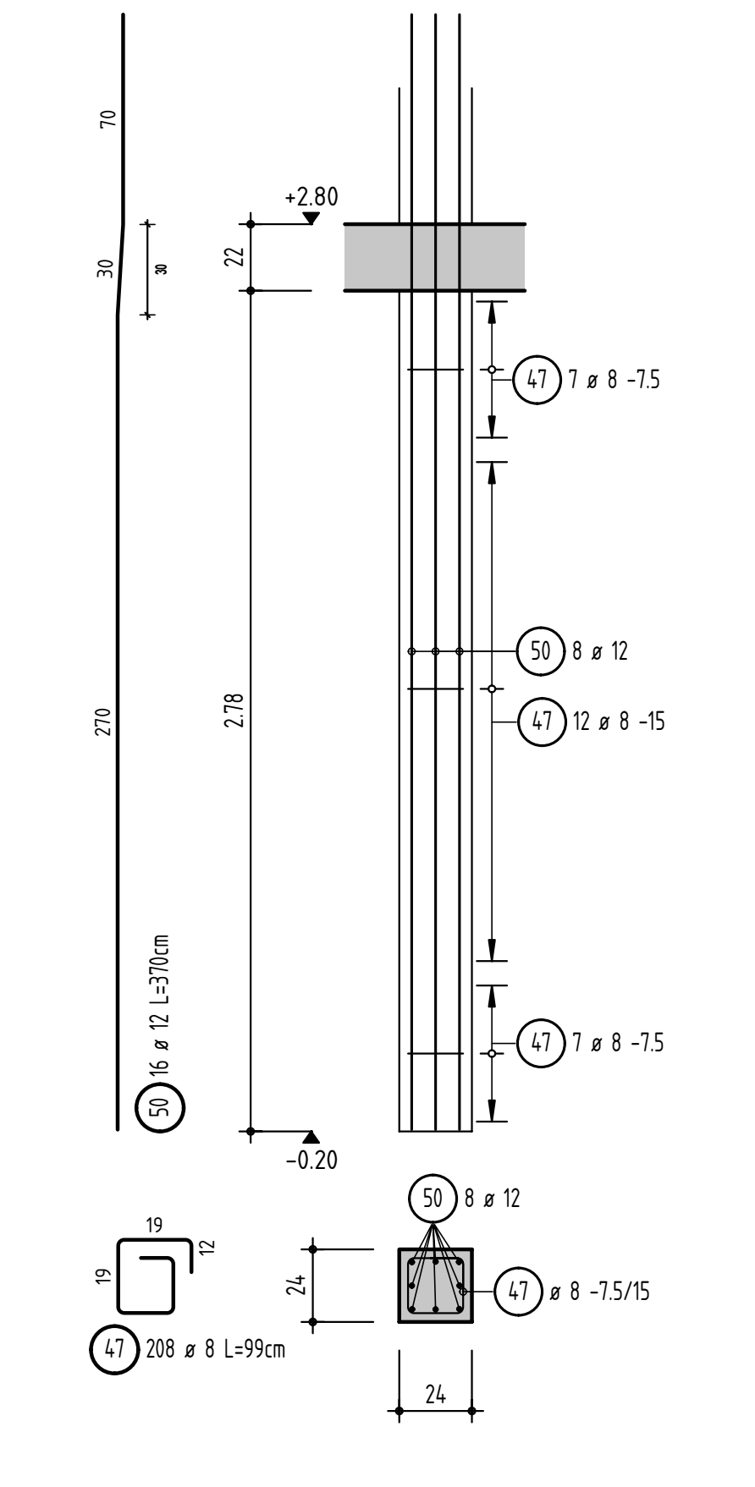

Pos. 1.2a Stb.-Stützen

b/d = 24/24cm M 1:25

6x ausführen

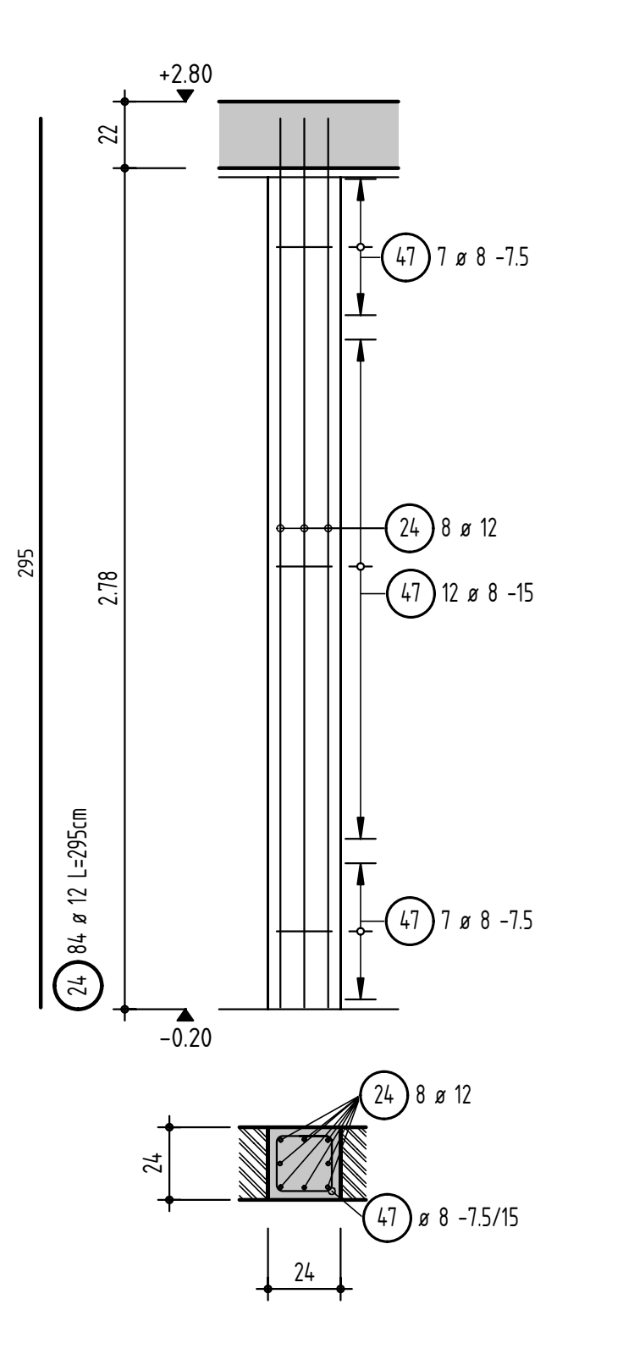

Pos. 1.3 Stb.-Stützen

b/d = 30/30cm M 1:25

2x ausführen

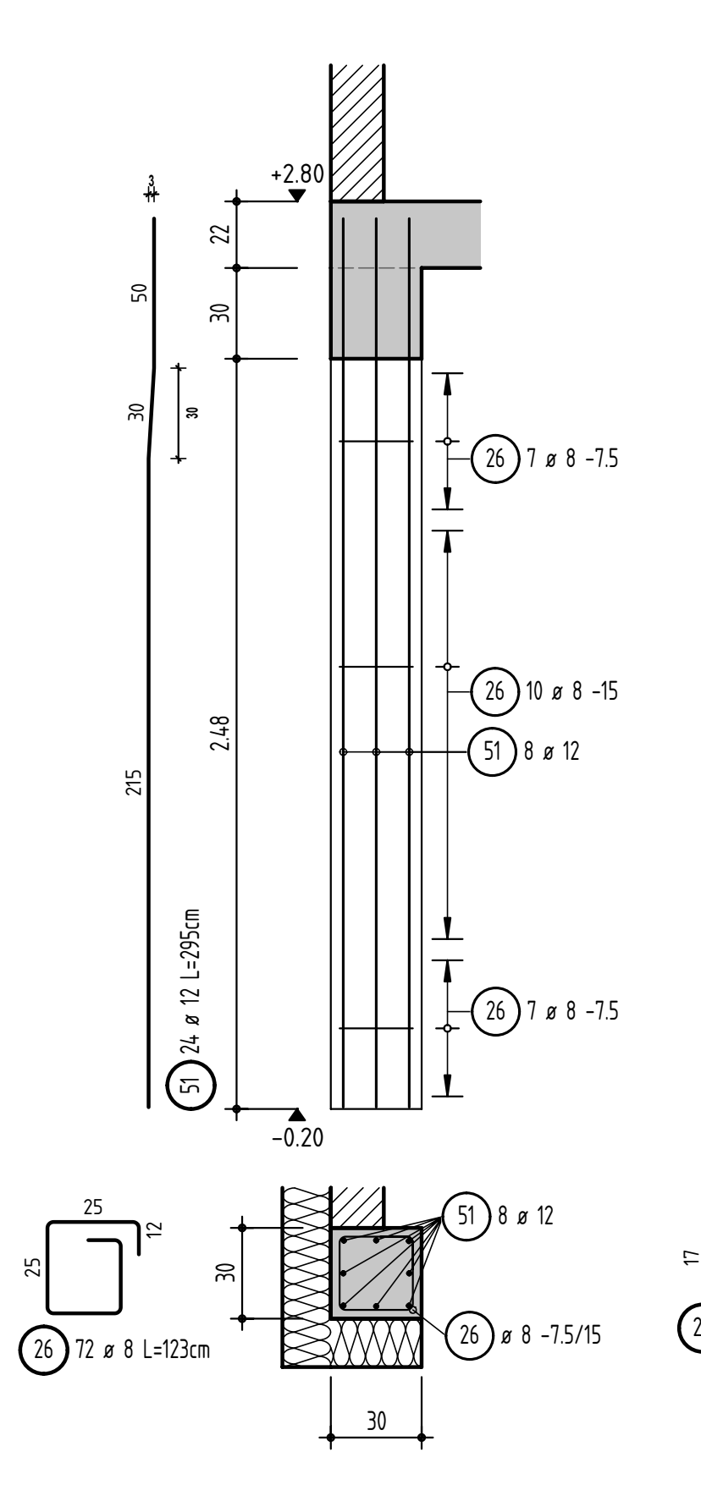

Pos. 1.3a Stb.-Stützen

b/d = 24/24cm M 1:25

2x ausführen

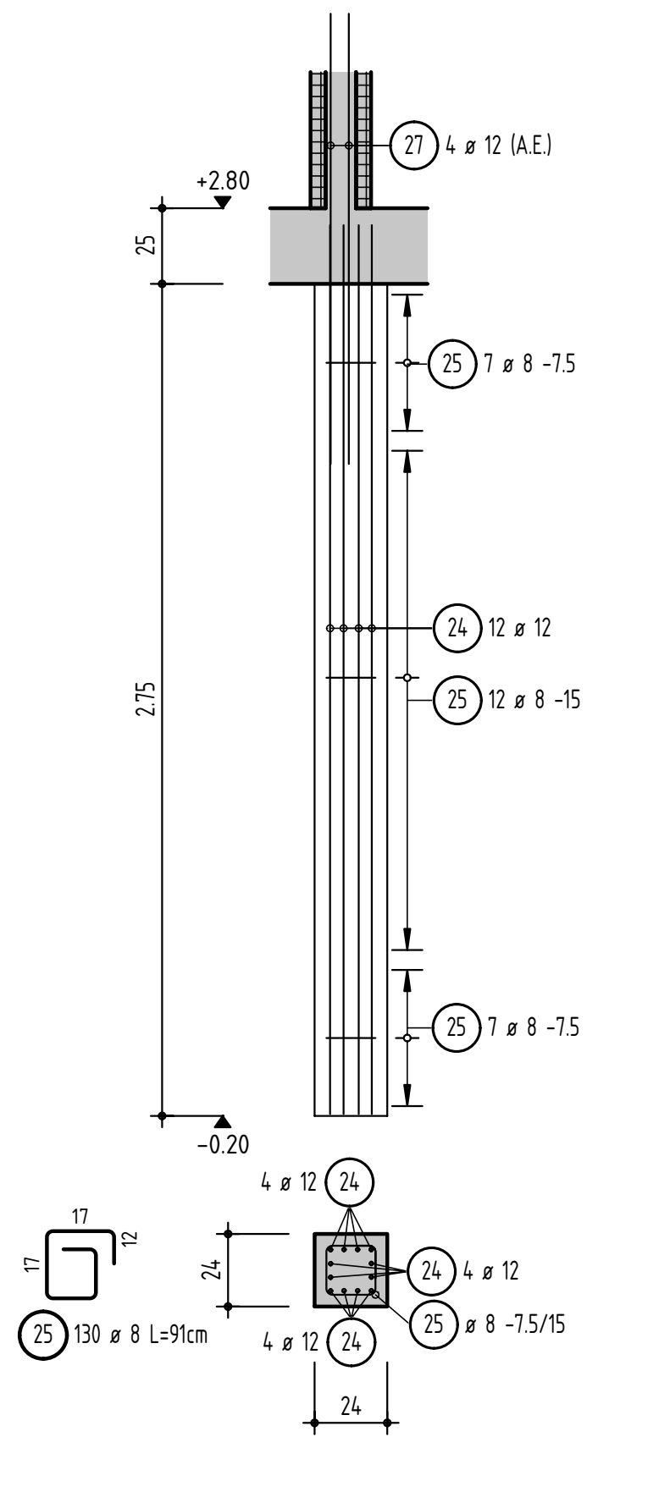

Pos. 1.3b Stb.-Stütze

b/d = 30/30cm M 1:25

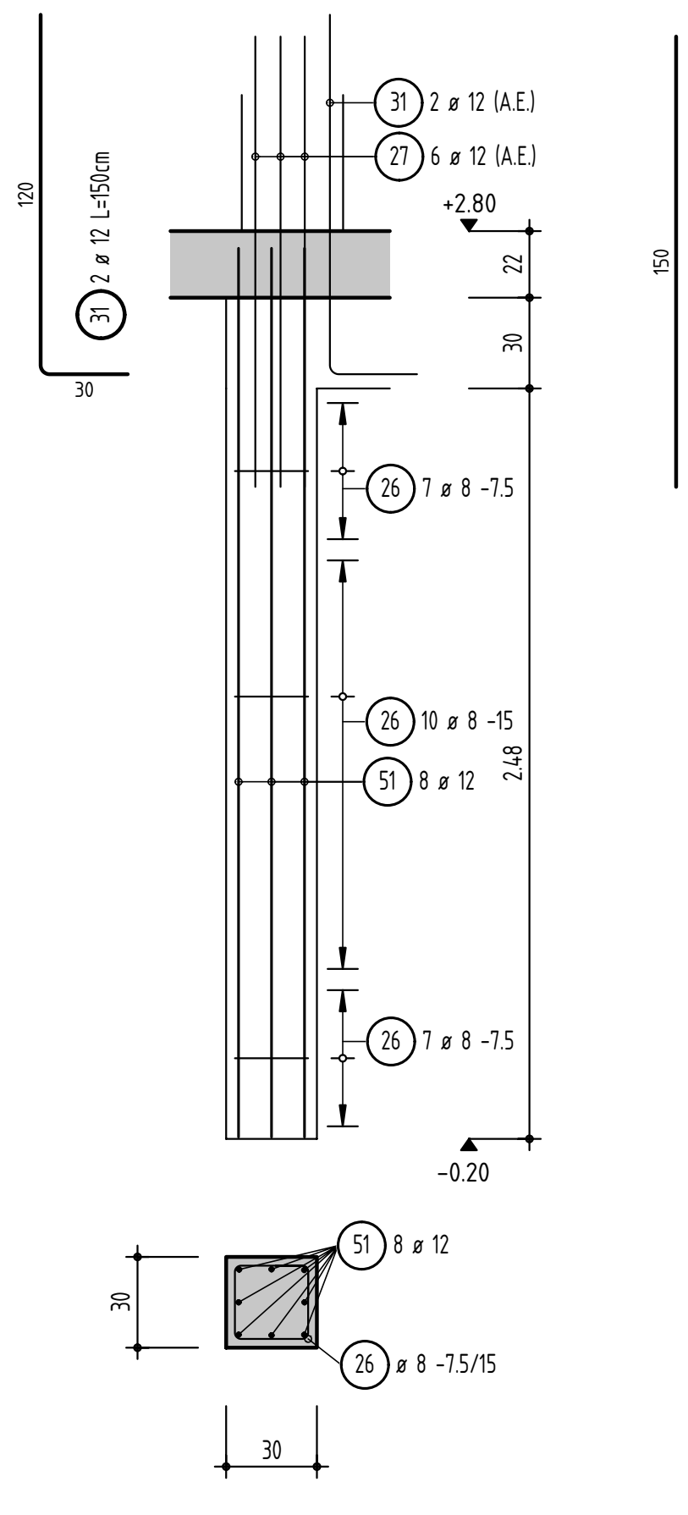

Pos. 1.4 Stb.-Stützen

b/d = 24/24cm M 1:25

3x ausführen

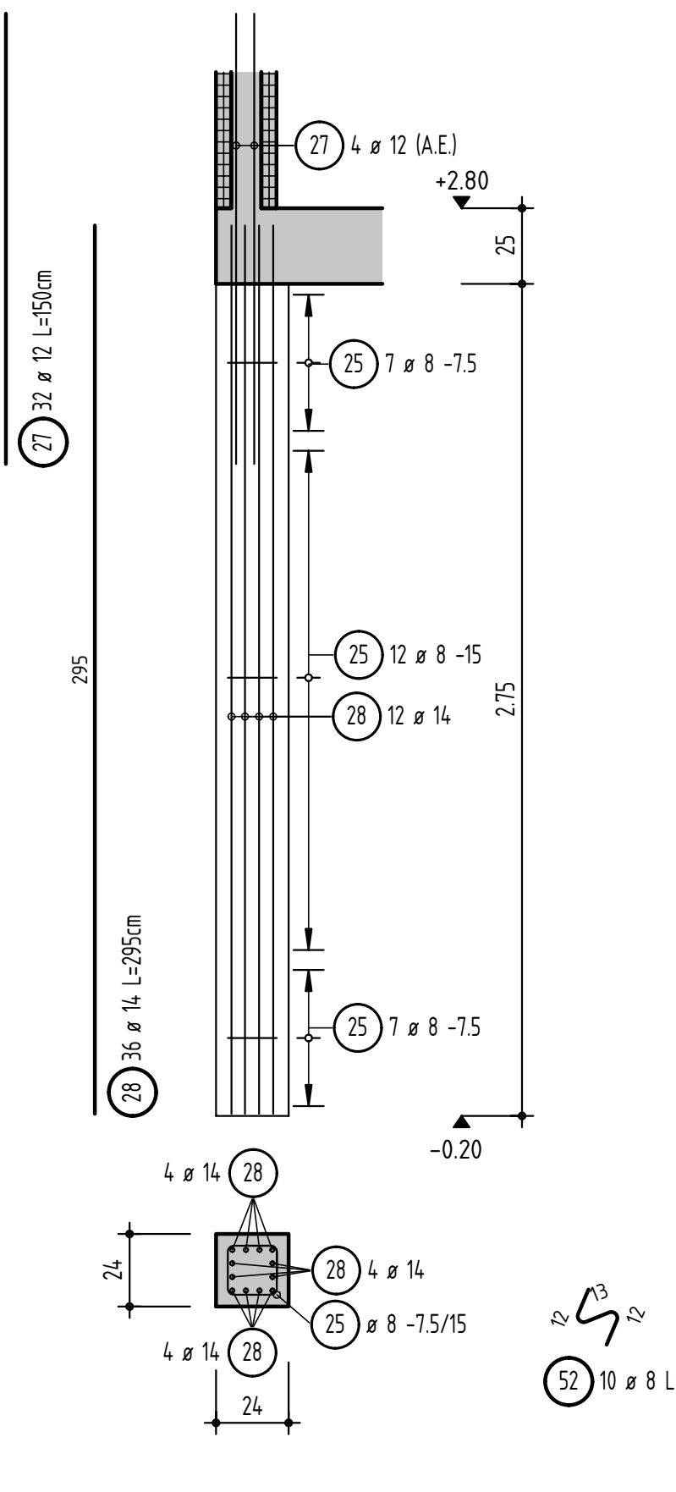

Pos. 1.5 Stb.-Stütze

b/d = 40/20cm M 1:25

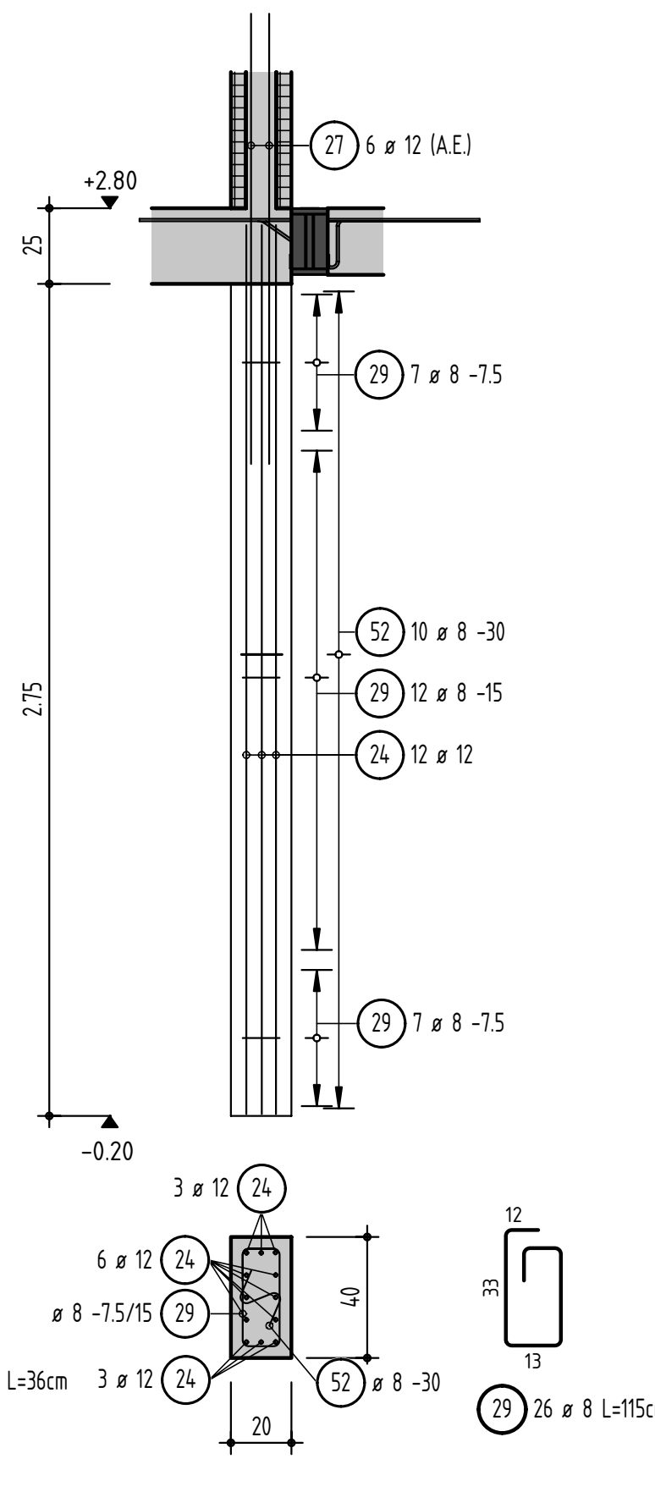

Schnitt 1-1 M 1:25

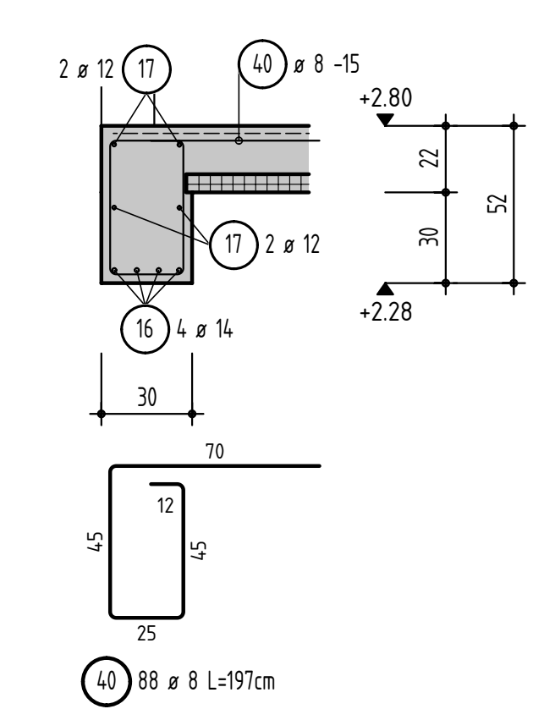

Schnitt 2-2 M 1:25

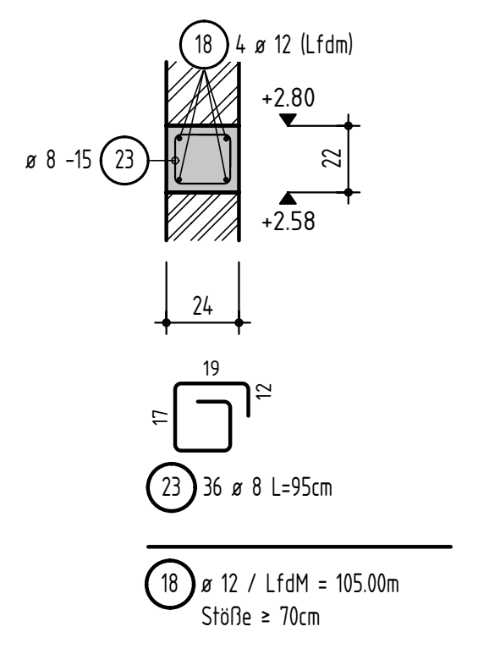

Schnitt 3-3 M 1:25

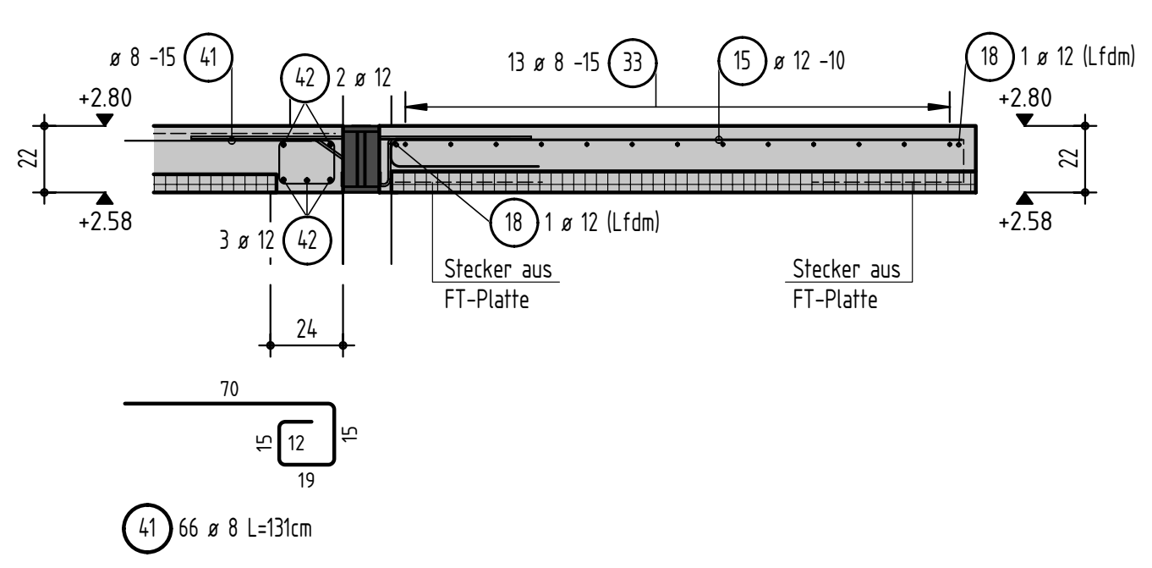

Schnitt 4-4 M 1:25

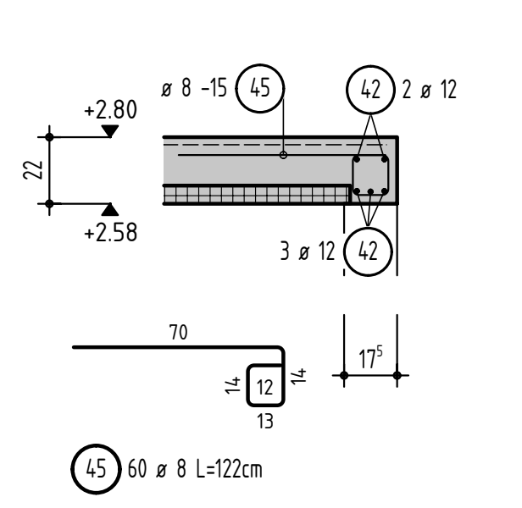

Schnitt 5-5 M 1:25

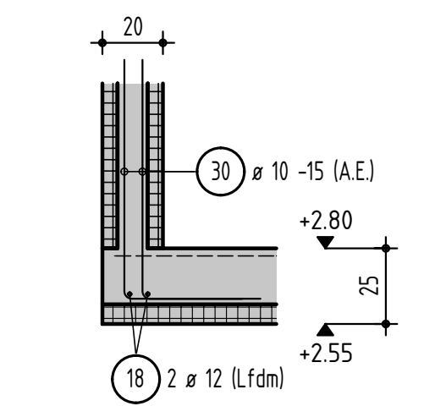

Schnitt 6-6 M 1:25

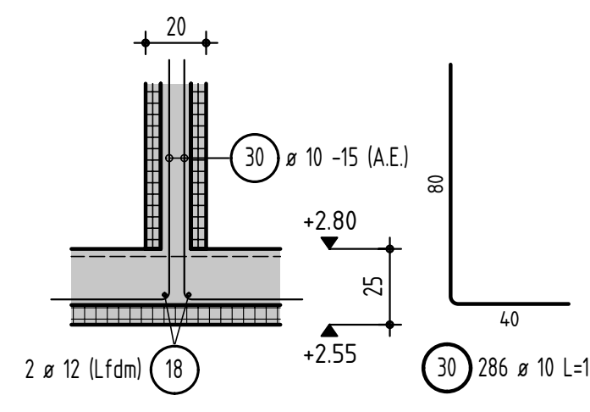

Schnitt 7-7 M 1:25

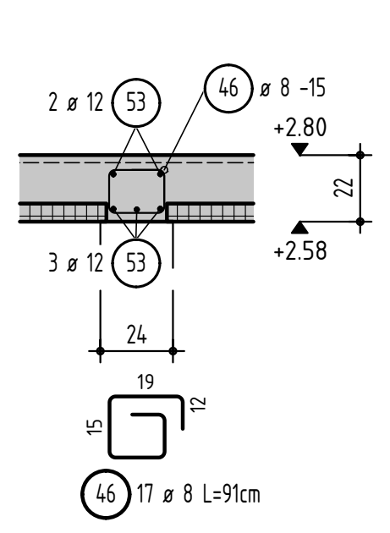

Schnitt 8-8 M 1:25

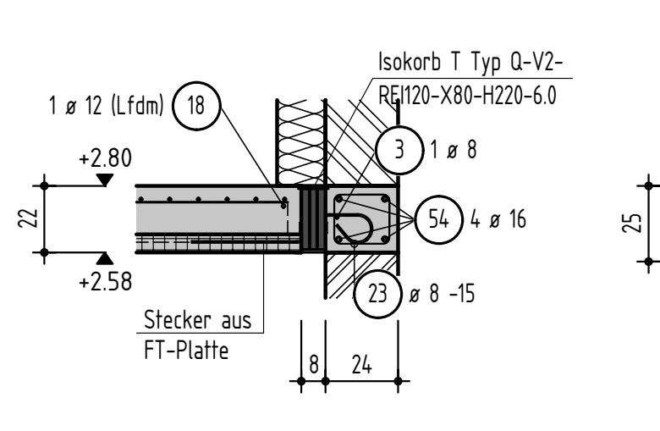

Schnitt 9-9 M 1:25

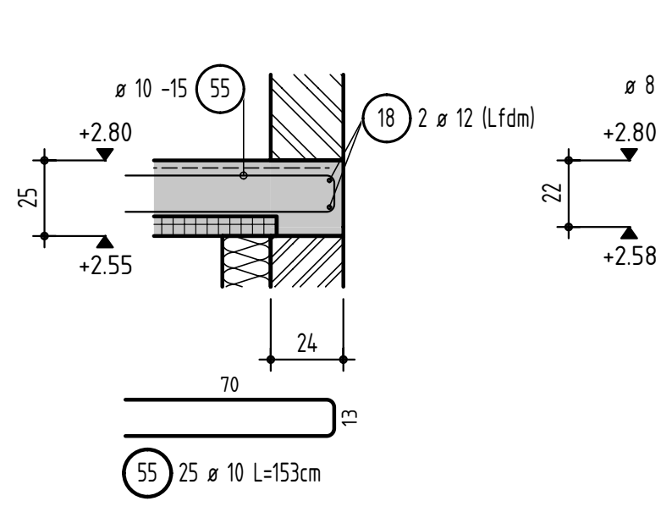

Schnitt 10-10 M 1:25

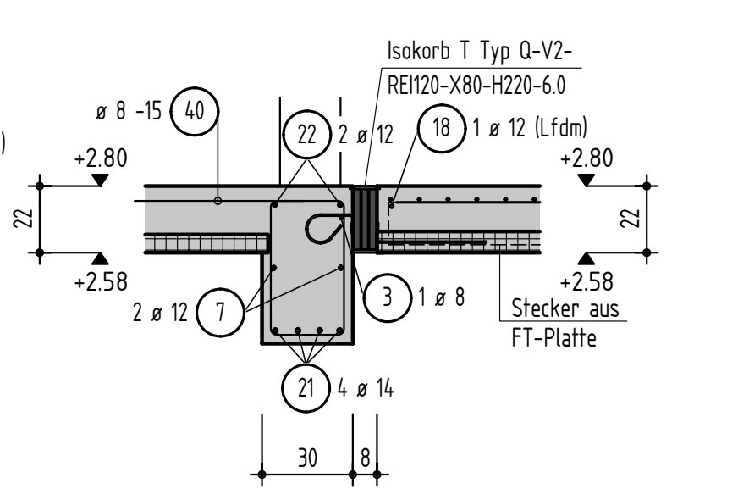

Alle Maße sind vor Arbeitsbeginn vom Unternehmer und Architekten auf Richtigkeit zu überprüfen

LAGENSCHEMA FÜR DECKENBEWEHRUNG:

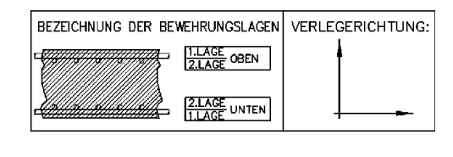

! UNFALLSCHUTZ !

GERADE NACH OBEN ENDENDE STÄBE (STECKEISEN) MÜSSEN ABGEDECKT ODER ZUSÄTZLICH HAKENFÖRMIG (OHNE VERRINGERUNG DER HAFTLÄNGE) ABGEBOGEN WERDEN.

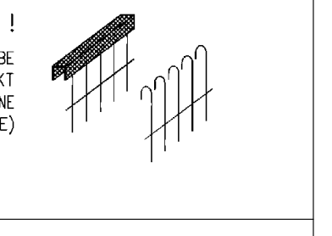

Betonstahl-und Spannstahlsorte: Betonstabstahl B500A , Betonstahlmatten B500A

ABKÜRZUNGEN

W: Wand
HW: Hohlwand
Bu: Bügel
A.E.: Anschlusseisen
Zul.: Zulage

LEGENDE

- ▩ STB-WÄNDE IN DER BETRACHTETEN EBENE
- ▨ STB-WÄNDE IN DER DARÜBERLIEGENDEN EBENE
- ▨ MAUERWERK KS-P RDK 2,0 D= 24cm
- ▨ MAUERWERK KS-P RDK 1,4 D= 17,5cm
- ▨ UNBEWEHRTE BETON
- ▨ WÄRMEDÄMMUNG

Biegen von Betonstählen nach DBV-Merkblatt "Betondeckung und Bewehrung 2011-01"

Bei der Bestimmung des Biegerollendurchmessers dbr ist DIN EN 1992-1-1/NA:2011-01, 8.3, EC 2 zu beachten und nach der bautechnischen Funktion der Biegung zu unterscheiden:

A) Biegung zur Kraftumleitung

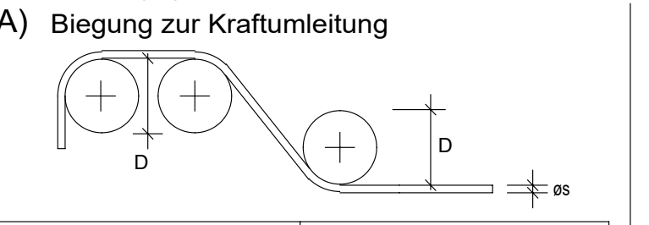

Mindestwerte der Betondecke rechtwinklig zur Krümmungsebene	Biegerollendurchmesser D [mm]
>100 mm und > 7 øs	min D = 10 øs
> 50 mm und > 3 øs	min D = 15 øs
≤ 50 mm und ≤ 3 øs	min D = 20 øs

Biegung nach A)

zur Herstellung und Überprüfung ist der erforderliche Biegerollendurchmesser immer anzugeben und zwar an der Biegeform im Bewehrungsplan und auf der Stabliste.

B) konstruktive Biegung

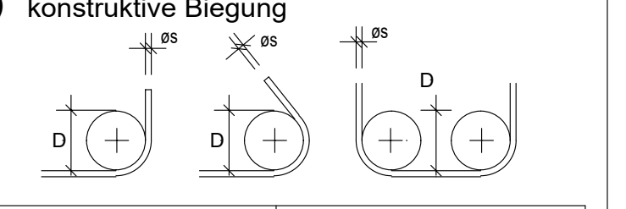

Stabdurchmesser øs [mm]	Biegerollendurchmesser D [mm]	
6, 8, 10, 12	4 øs	min D = 40 mm
14, 16	4 øs	min D = 64 mm
20, 25, 28	7 øs	min D =175 mm

Biegung nach B)

wird an der Biegeform weder im Bewehrungsplan noch auf der Stabliste ein Biegerollendurchmesser angegeben, so ist erf. dbr in Abhängigkeit von der obigen Tabelle zu entnehmen.

Bei Betonstahlmatten und geschweißter Bewehrung, die nach dem Schweißen gebogen werden, ist zusätzlich DIN EN 1992-1-1/NA:2011-01, Tab NA.8.1.b zu beachten. Die unter A) und B) aufgeführten Mindestwerte der Biegerollendurchmesser gelten nur, wenn a≥ 4ds (a=Abstand der Schweißung vom Krümmungsbeginn).

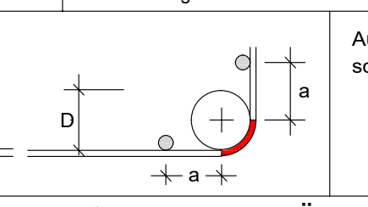

Ausführung von Bügelschlössern bei Stützen:

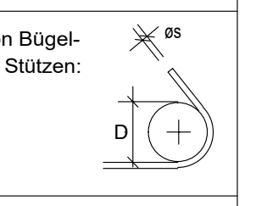

DIESER PLAN HAT NUR IM ZUSAMMENHANG MIT DEN PLÄNEN DES ARCHITEKTEN GÜLTIGKEIT. UNSTIMMIGKEITEN SIND VORAB MIT DER BAULEITUNG ZU KLÄREN.

Grundlage: Architekturplan

INDEX	DATUM	ART DER ÄNDERUNG	gez.:
01A	10.10.2024	Erstellung	P.Vid.
02A	18.10.2024	Isokörbe angepasst	P.Vid.

PLANERSTELLER :

Thanh Huynh
Düsseldorf
Tel.: 0163 9654179
E-mail: thanh.huynh@th-bau.com

THANH HUYNH
Ingenieurbüro

BAUHERR :

Herr Max Mustermann
Musterstr., 44892 Bochum

BAUVORHABEN :

Neubau einer Wohn- und Büroanlage
Maxmustermannstr.1A

BAUTEIL :

BEWEHRUNG DECKE Ü. ERDGESCHOSS UND STÜTZEN
GRUNDRISS + SCHNITTE

FREIGABEN :

Archtitekt am ________________________.

Prüfingenieur am ________________________.

Plannummer : KEP_BP_GR_EG_02A

PROJEKT-NR. 004

Gezeichnet : P.Vid.
Maßstab : 1:25/50
Datum : 10.10.2024
Codierung : Projekt_Planart_Layout_Geschoss_Index